

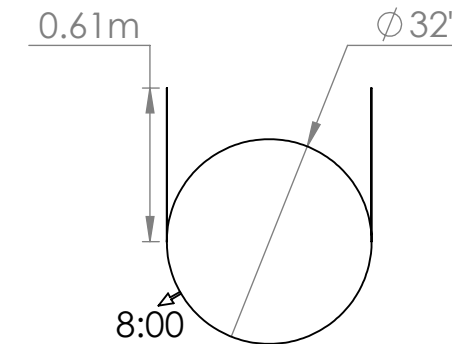
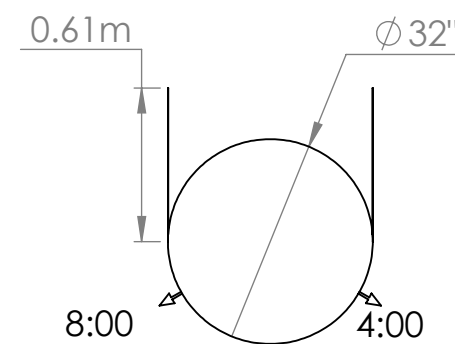
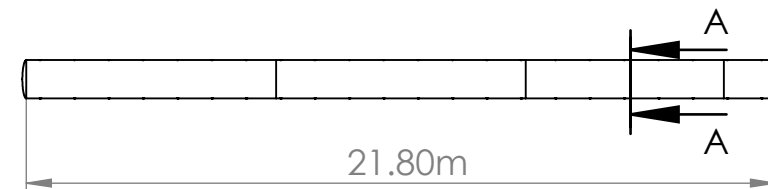
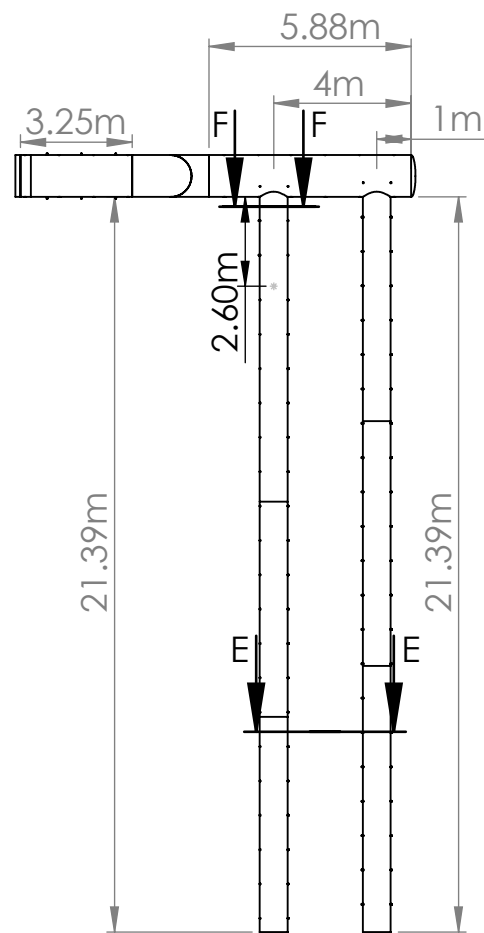



VISTA SUPERIOR

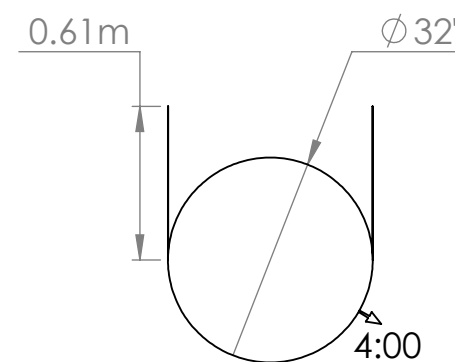

SECCIÓN E-E
ESCALA 1 : 30

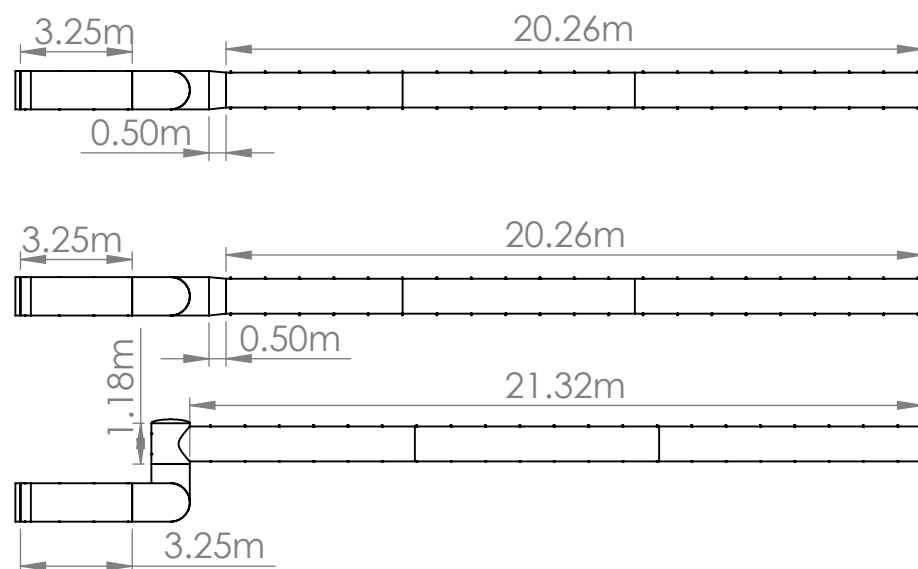

SECCIÓN F-F

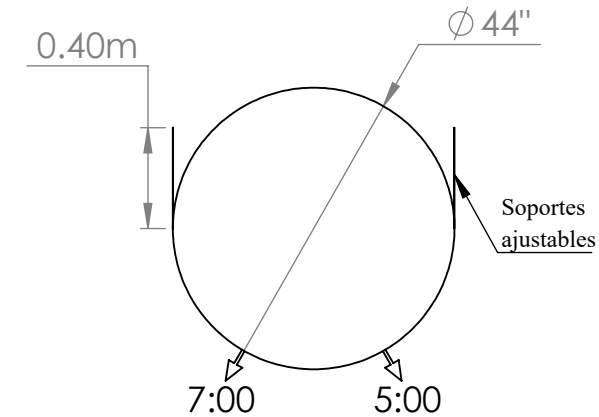

SECCIÓN A-A

Cliente:

Vernel Industrias

Proyecto:	DTI-251443-2026
-----------	------------------------

Responsable: **Ana Raya**

Elaboró:

Antonio Vázquez

Fecha:
20/08/2026 /Rev. D

Tipo de difusión: **MultiFlow**

No. de líneas de difusión:

Indicadas

Ubicación:	Indicada
------------	-----------------

Soportes:	9:00 y 3:00
-----------	--------------------

Material: **Poly 4 NAC**

Color: **White**





Aplicación extra:

Antibacterial

Altura de diseño:	7 m.
-------------------	-------------



VISTA LATERAL

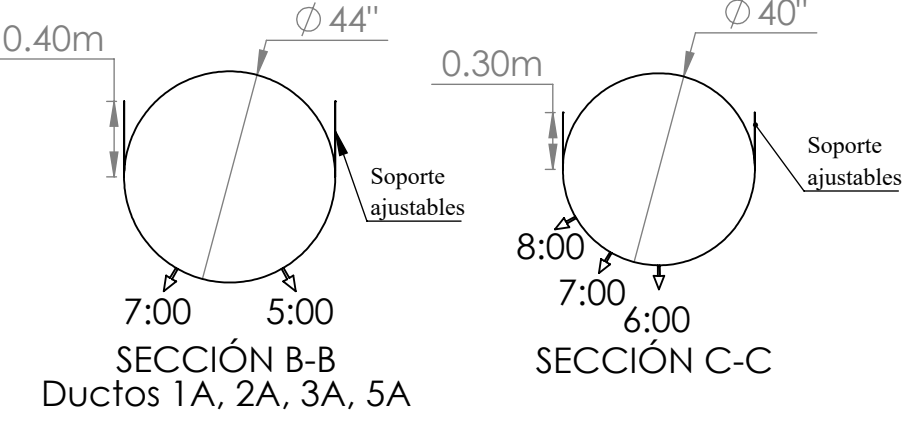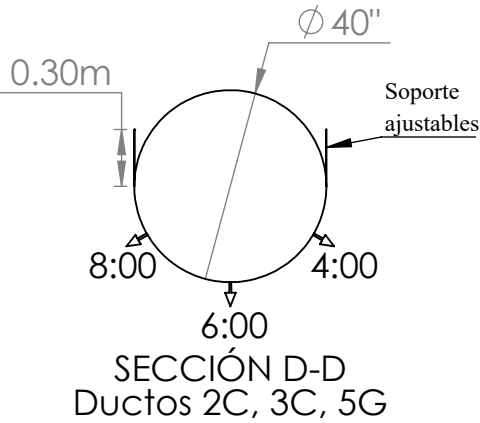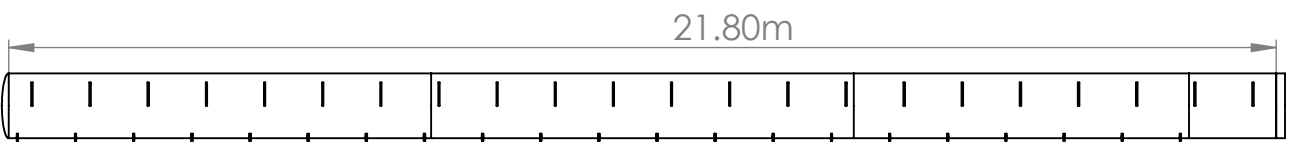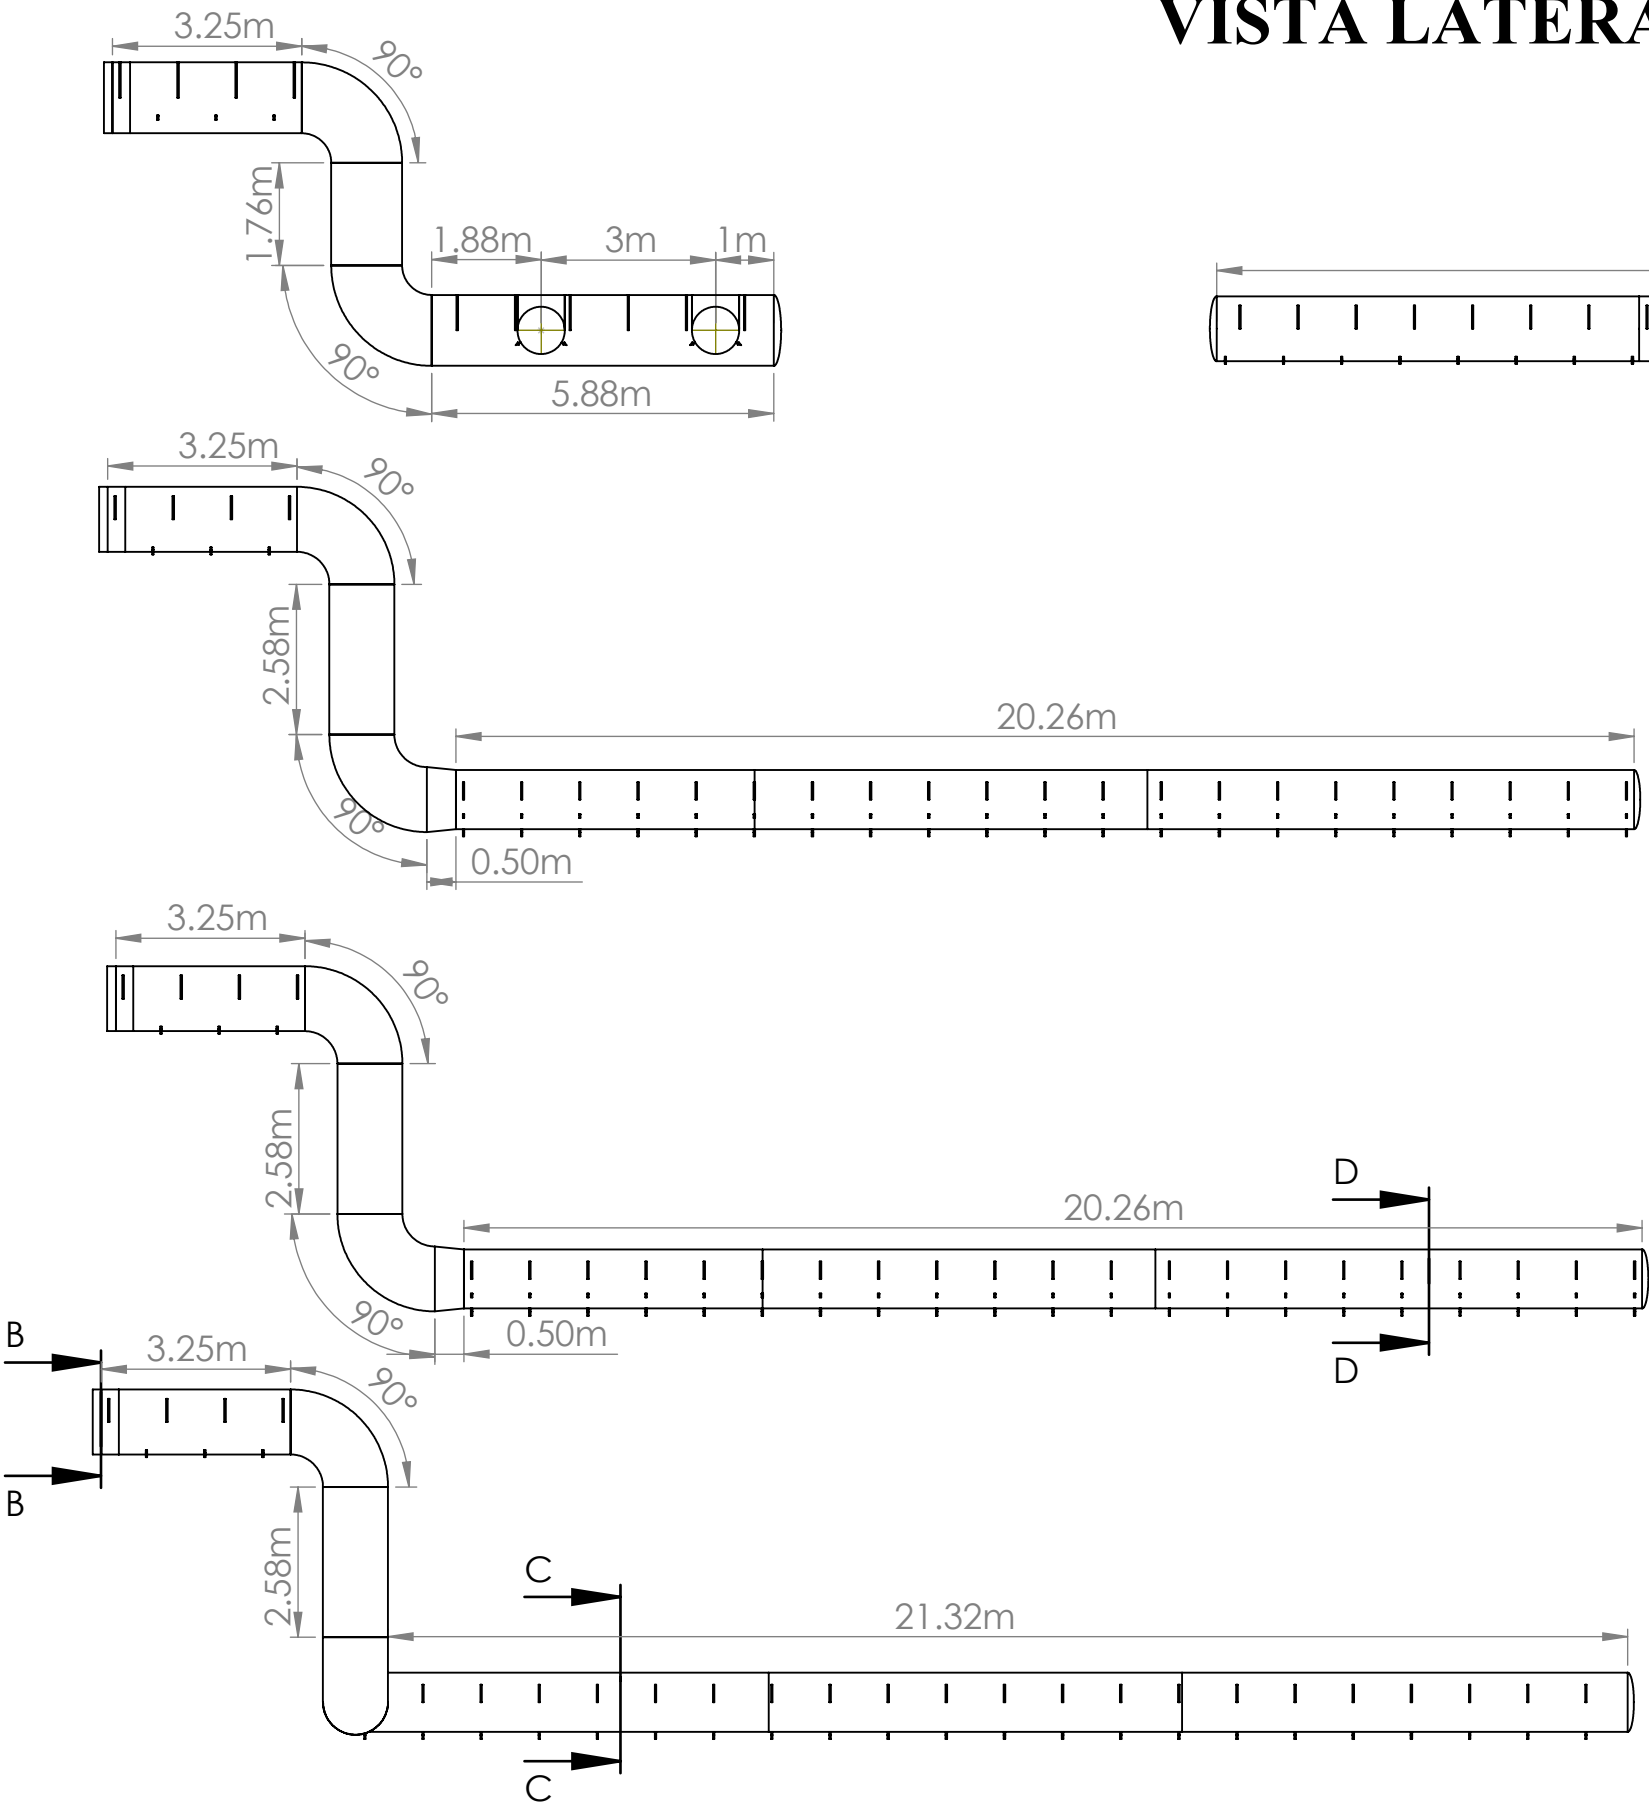

Cliente:
Vernel Industrias

Proyecto:
DTI-251443-2026

Responsable:
Ana Raya

Elaboró:
Antonio Vázquez

Fecha:
20/08/2026 /Rev. D

Tipo de difusión:
MultiFlow

No. de líneas de difusión:
Indicadas

Ubicación:
Indicada

Soportes:
9:00 y 3:00

Material:
Poly 4 NAC




Color:
White

Aplicación extra:
Antibacterial



Altura de diseño:
7 m.



VISTA SUPERIOR

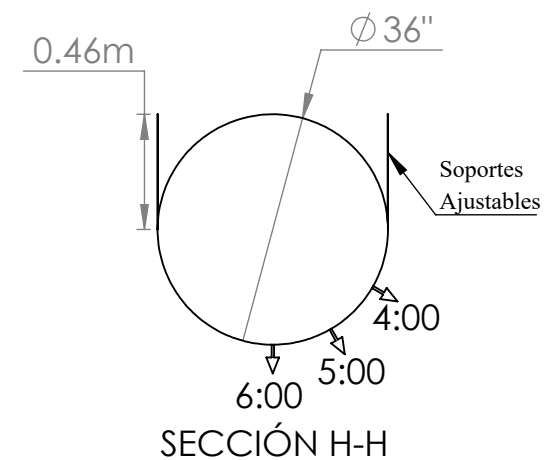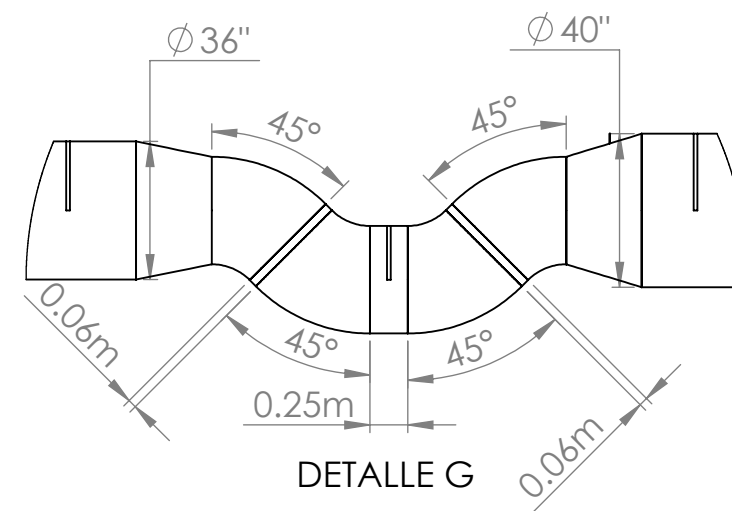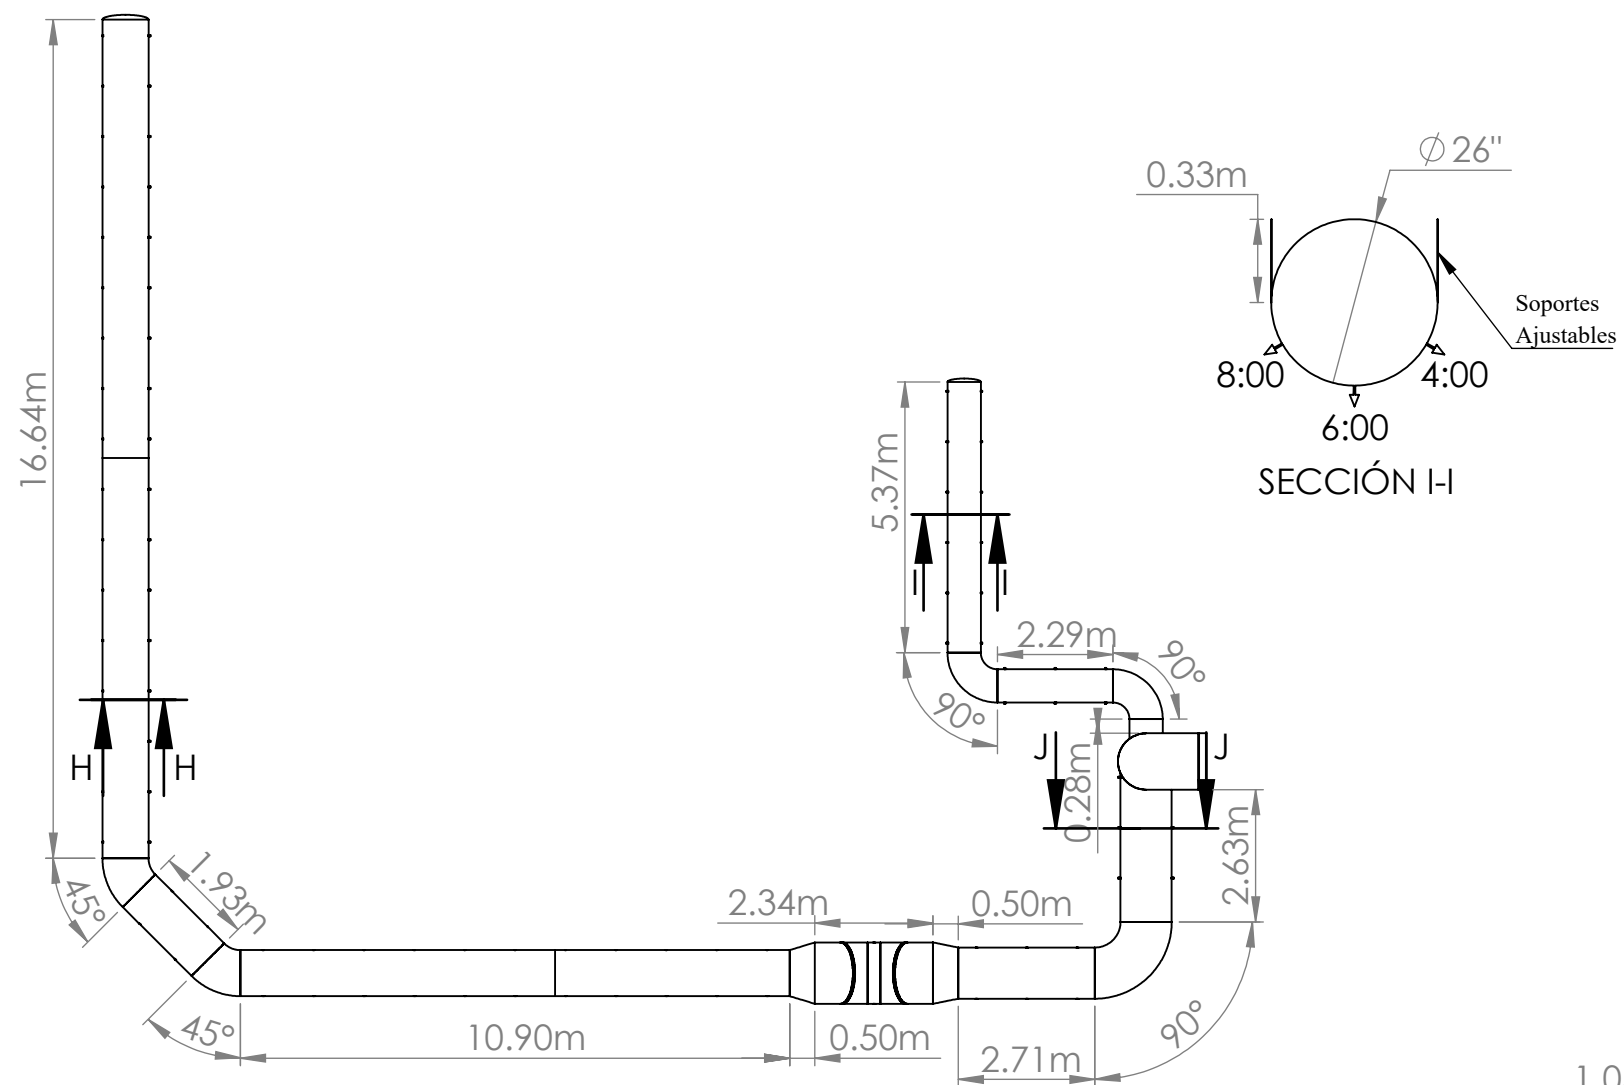

VISTA LATERAL

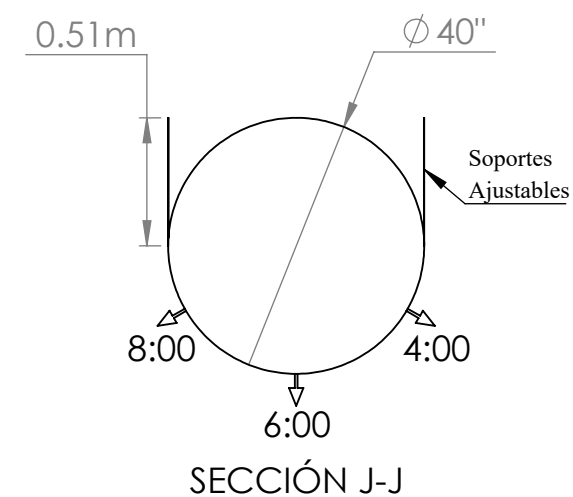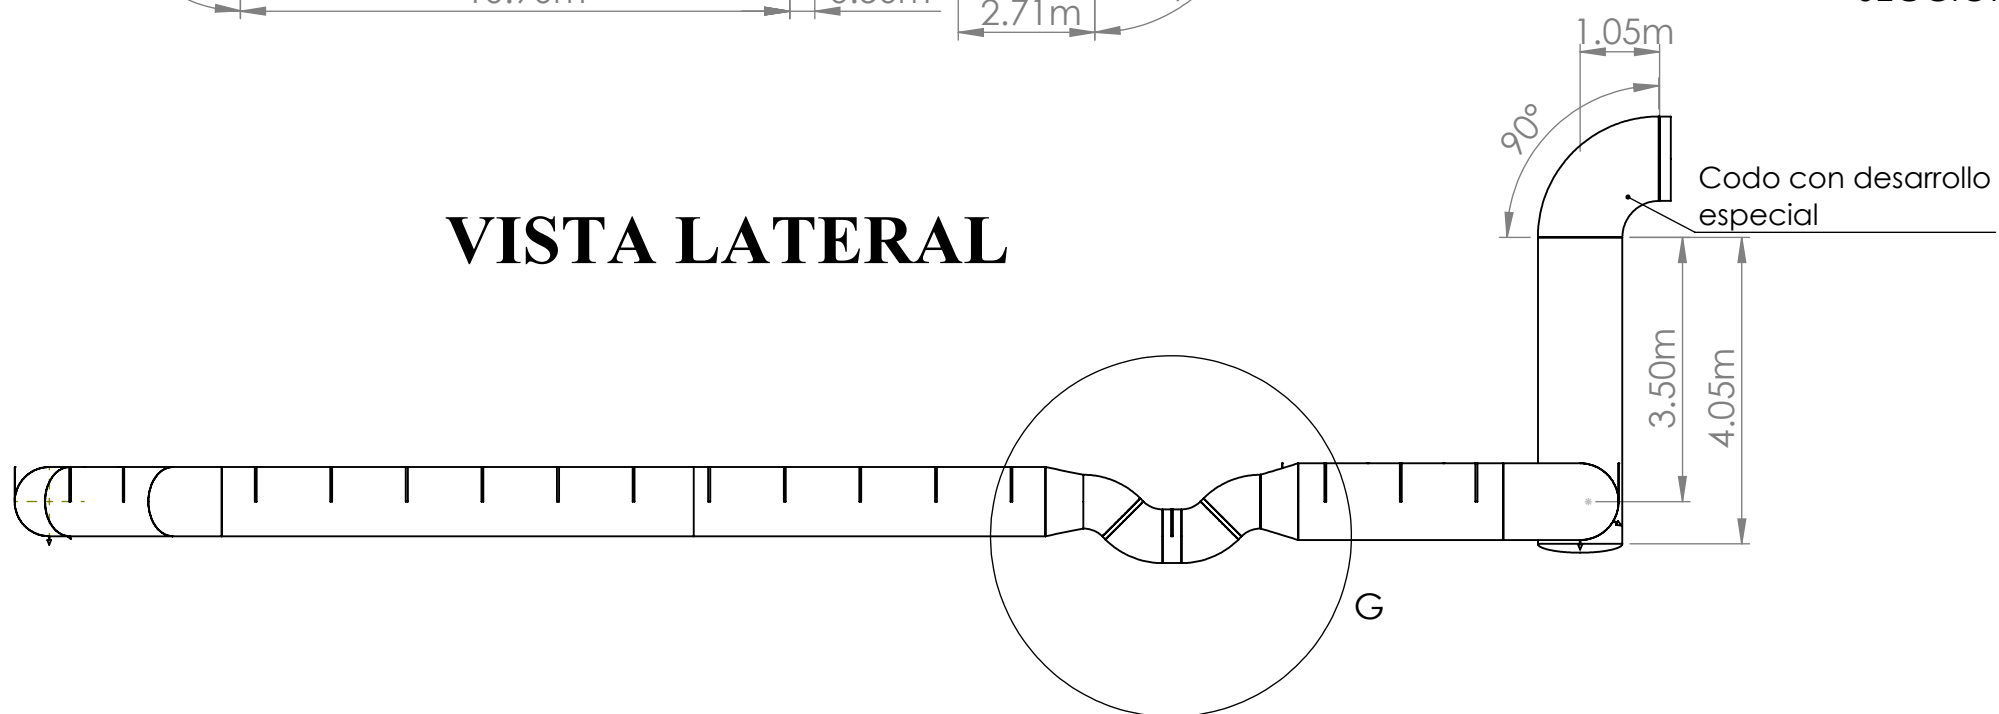

Cliente:

Vernel Industrias

Proyecto:	DTI-251443-2026
-----------	------------------------

Responsable:	Ana Raya
--------------	-----------------

Elaboró:

Antonio Vázquez

Fecha: **20/08/2026 /Rev. D**

Tipo de difusión: **MultiFlow**

No. de líneas de difusión:

Indicadas

Ubicación:	Indicada
------------	-----------------

Soportes:	9:00 y 3:00
-----------	--------------------

Material: **Poly 4 NAC**

Color: **White**



Aplicación extra:

Antibacterial

Altura de diseño:	7 m.
-------------------	-------------



VISTA ISOMÉTRICA

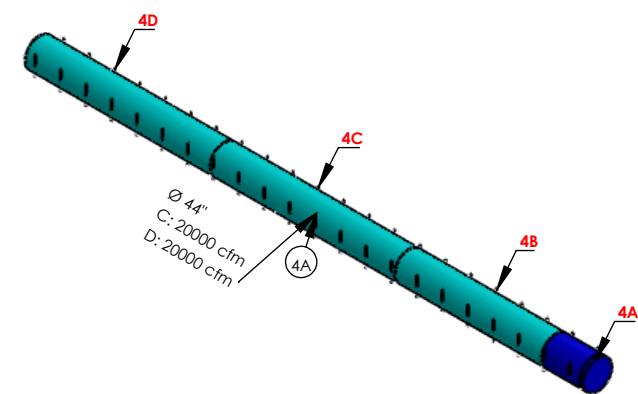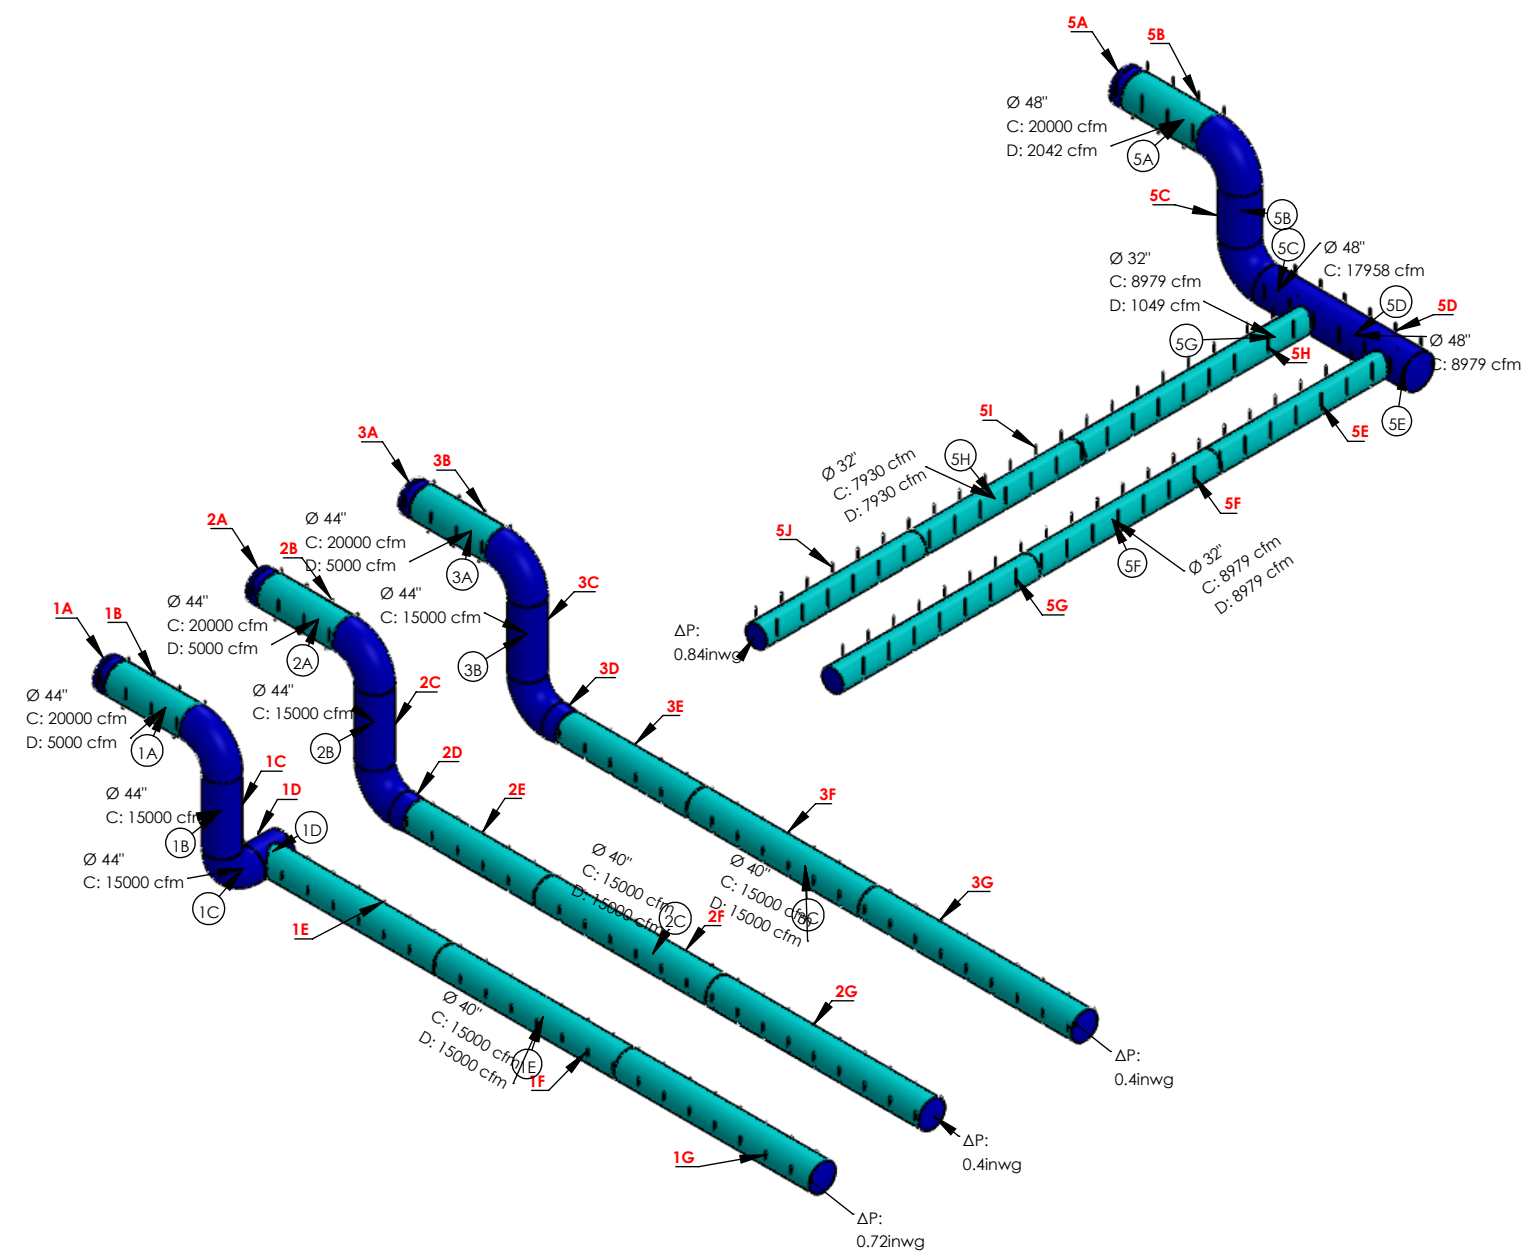

Cliente:
Vernel Industrias

Proyecto:
DTI-251443-2026

Responsable:
Ana Raya

Elaboró:
Antonio Vázquez

Fecha:
20/08/2026 /Rev. D

Tipo de difusión:
MultiFlow

No. de líneas de difusión:
Indicadas

Ubicación:
Indicada

Soportes:
9:00 y 3:00

Material:
Poly 4 NAC

Color:
White

Aplicación extra:
Antibacterial

Altura de diseño:
7 m.



